


Symbol	Name
	Inverter
	Isolator Without Earth Switch
	CT
	High Voltage CB
	Isolator with Earth Switch
	Low Voltage CB

Indoor: Main Substation Building

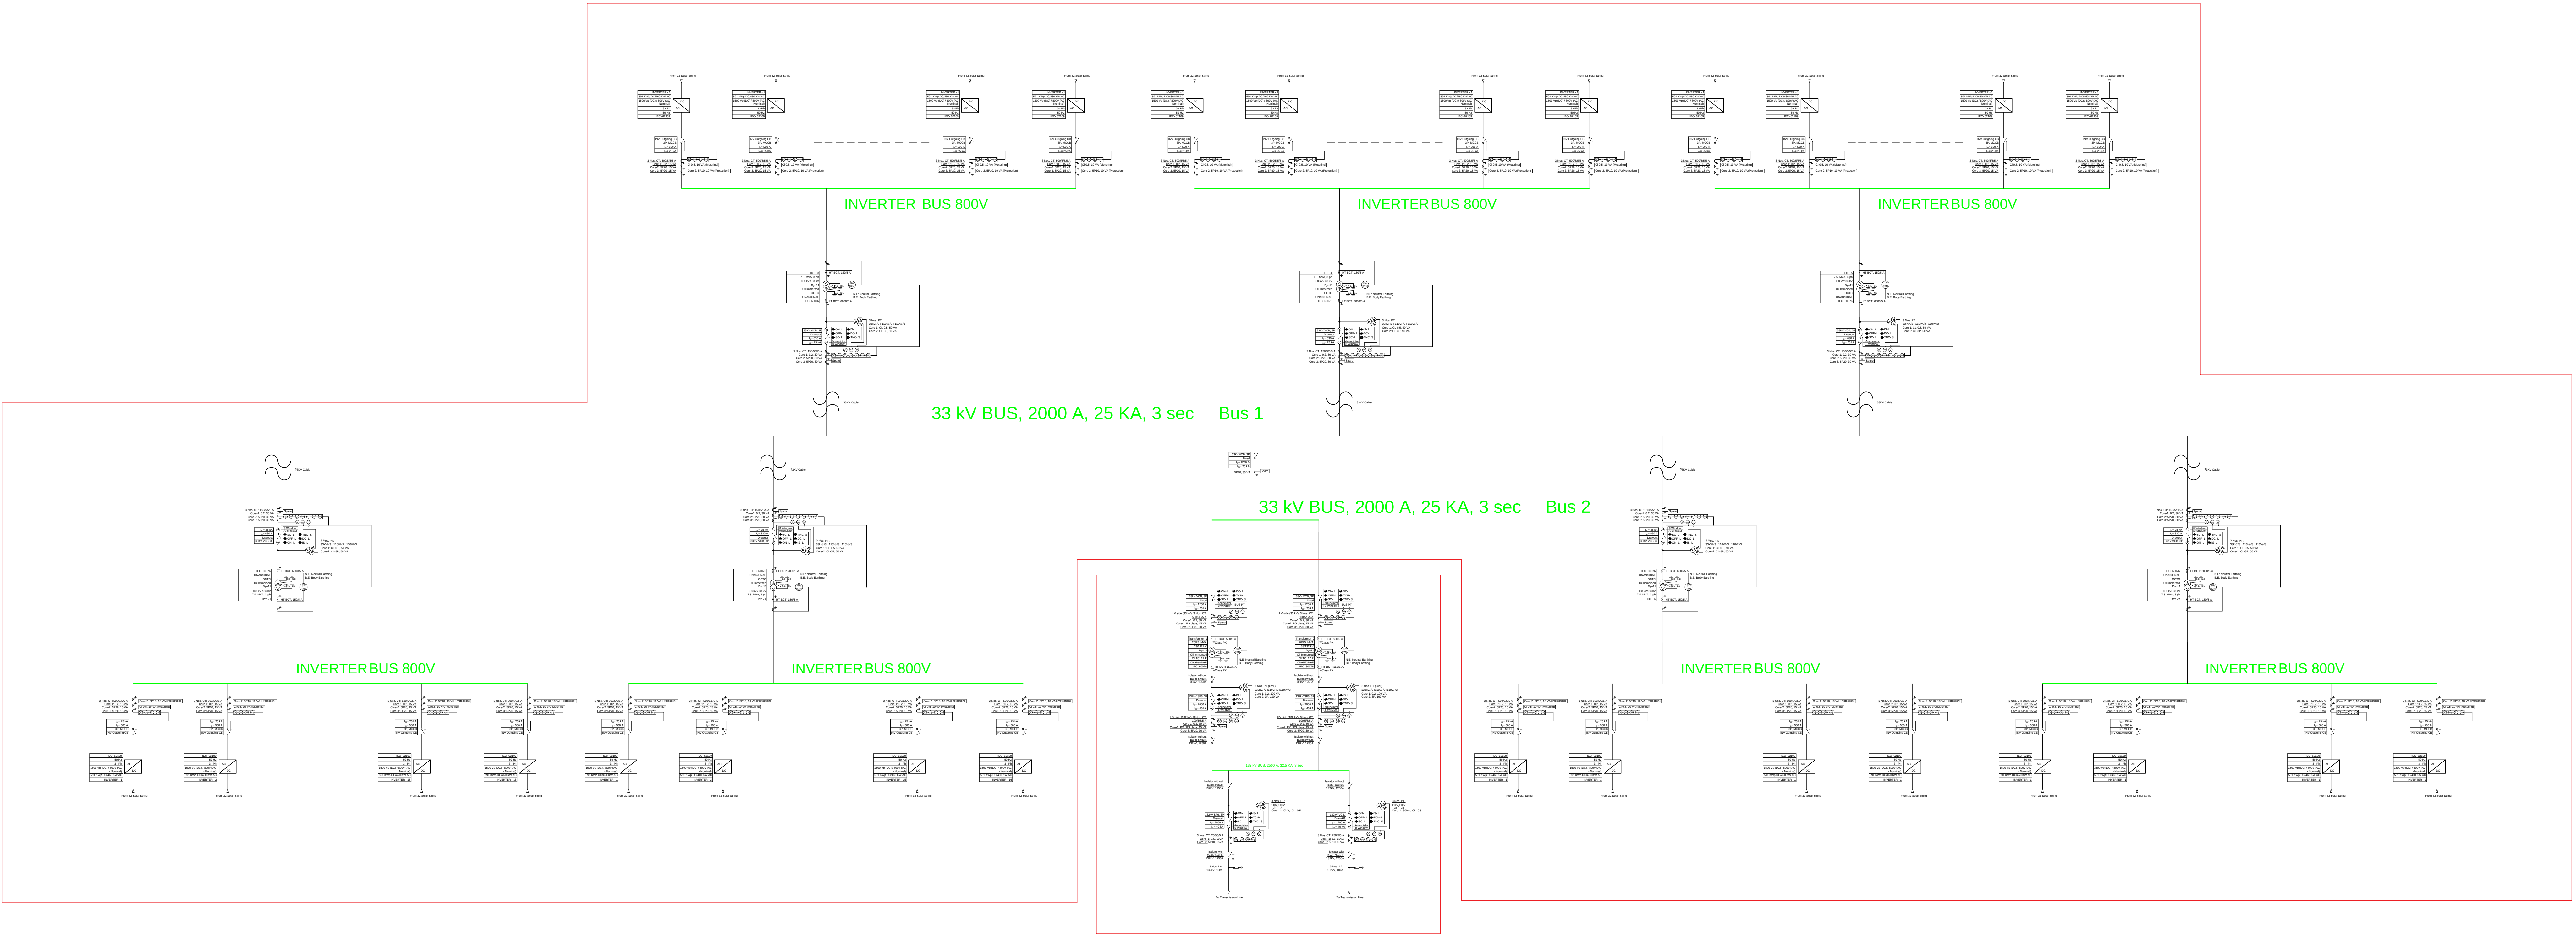

Outdoor Switchyard

Client	
Sponsor	
Project Title	Fatikchari 45 MW AC Grid-Conneted Solar Power Plant
Drawing Title	Single Line Diagram with Protection Scheme
Designed By	Fahim Faisal CUET EEE 18 Abtahi Power and Automation Graduate Trainee Engineer
Sheet No.	1 of 1
Date	6/25/2026